Painéis de stock utilizados	2
Área total utilizada	60210.25 59%
Área total desperdiçada	40989.75 41%
Cortes totais	16
Comprimento de corte total	1964
Espessura de corte	0

Painéis 121.5×28.5 x1 \ 76.5×69.5 x1 \ 106.5×37.5 x1 \ 37.5×30 x1 \ 153.5×37.5 x1 \ 153.5×69.5 x1 \ 86×37.5 x1 \ 54×37.5 x1 \ 150×75 x1 \ 150×28.5 x1 \ 121.5×75 x1

Stock 275×184 x2

Painel de stock	275×184
Área utilizada	43879 87%
Área excedente	6721 13%
Cortes	11
Comprimento de corte	1385.5
Painéis	8
Excedentes	4

Painel	Qtd
121.5×28.5	1
69.5×76.5	1
30×37.5	1
153.5×37.5	1
153.5×69.5	1
54×37.5	1
75×150	1
28.5×150	1

#	Painel	Corte	Result
1	275×184	y=153.5	- \ -
2	153.5×184	x=69.5	153.5×6 \ -
3	153.5×114.5	x=37.5	153.5×3 \ -
4	153.5×77	x=76.5	- \ surplus
5	153.5×76.5	y=69.5	69.5×76 \ -
6	121.5×184	x=150	- \ -
7	121.5×150	y=75	75×150 \ -
8	46.5×150	y=28.5	28.5×15 \ surp
9	121.5×34	x=28.5	121.5×2 \ surp
10	84×76.5	x=37.5	- \ surplus
11	84×37.5	y=54	54×37.5 \ surp

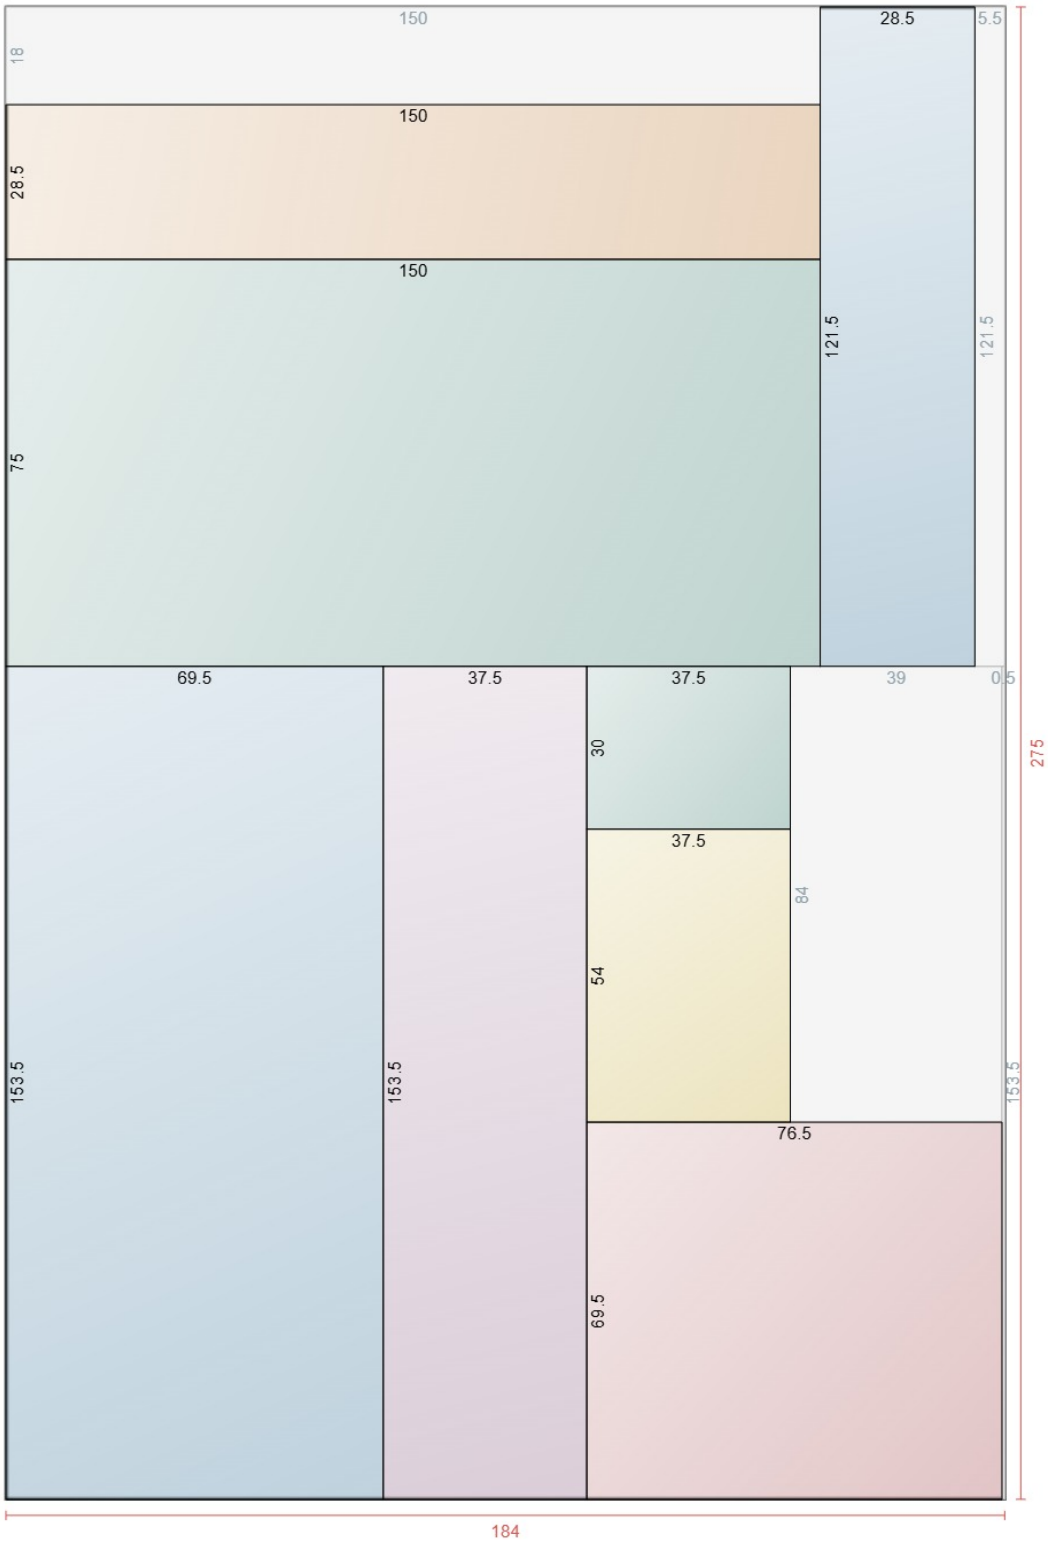

Painel de stock	275×184
Área utilizada	16331.25 32%
Área excedente	34268.75 68%
Cortes	5
Comprimento de corte	578.5
Painéis	3
Excedentes	3

Painel	Qtd
106.5×37.5	1
86×37.5	1
121.5×75	1
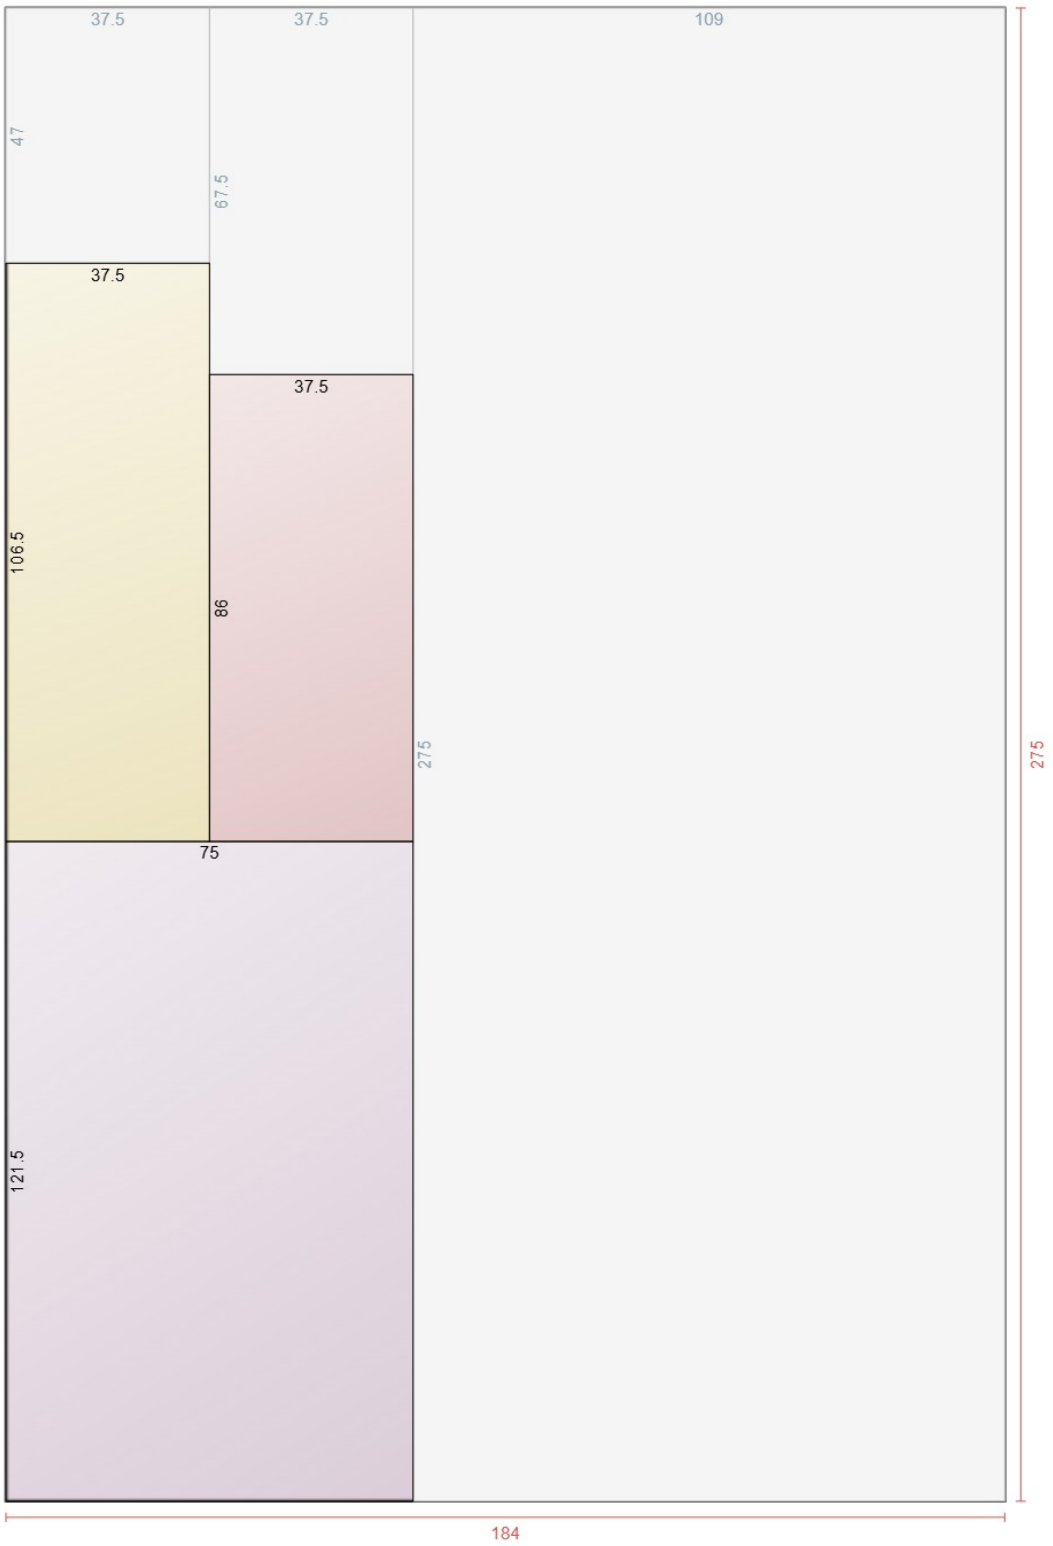
#	Painel	Corte	Result
1	275×184	x=75	- \ surplus
2	275×75	y=121.5	121.5×7 \ -
3	153.5×75	x=37.5	- \ -
4	153.5×37.5	y=106.5	106.5×3 \ surplus
5	153.5×37.5	y=86	86×37.5 \ surplus